

WORTHINGTON PHASE II

REVISED PRELIMINARY PLAT

CITY OF NORTH ROYALTON
COUNTY OF CUYAHOGA, STATE OF OHIO
PART OF ORIGINAL ROYALTON TOWNSHIP SECTION No. 2



OWNER

PRIDE ONE
387 MEDINA ROAD
SUITE 600
MEDINA, OHIO 44256
PAT RAKOCI
(330) 590-8014

DEVELOPER

PRIDE ONE
387 MEDINA ROAD
SUITE 600
MEDINA, OHIO 44256
PAT RAKOCI
(330) 590-8014

SITE INFORMATION

WORTHINGTON PHASE II:
PPN: 481-21-015
TOTAL AREA: 30.97 AC
SUBLOTS: 13.97 AC
ROW: 1.78 AC
OPEN SPACE & PARK:
OPEN SPACE: 5.13 AC
CITY PARK: 3.41 AC
8.54 AC (27.6%)
FUTURE DEVELOPMENT: 6.68 AC
PROPOSED SUBLOTS: 31
PROPOSED ROAD LENGTH: 1215 LF
WORTHINGTON PHASE I:
OPEN SPACE (PREVIOUSLY ROW): 0.29 AC


R1-B ZONING INFORMATION

SINGLE FAMILY DWELLINGS

MAX. DENSITY: 2.4 UNITS PER AC
MIN. LOT SIZE: 15,600 SF
MIN. LOT WIDTH AT SETBACK LINE: 80'
MIN. SETBACK FROM R.O.W.: 50'
MIN. SIDE YARD: 8'
MIN. REAR YARD: 50'
MAX. BUILDING HEIGHT: 2-STORIES

VARIANCE

1246.02 STREETS
(h) CUL-DE-SACS:
STATES: MAX. LENGTH 600'
PROPOSED: 3518' (2303' EXISTING + 1215' PROPOSED)

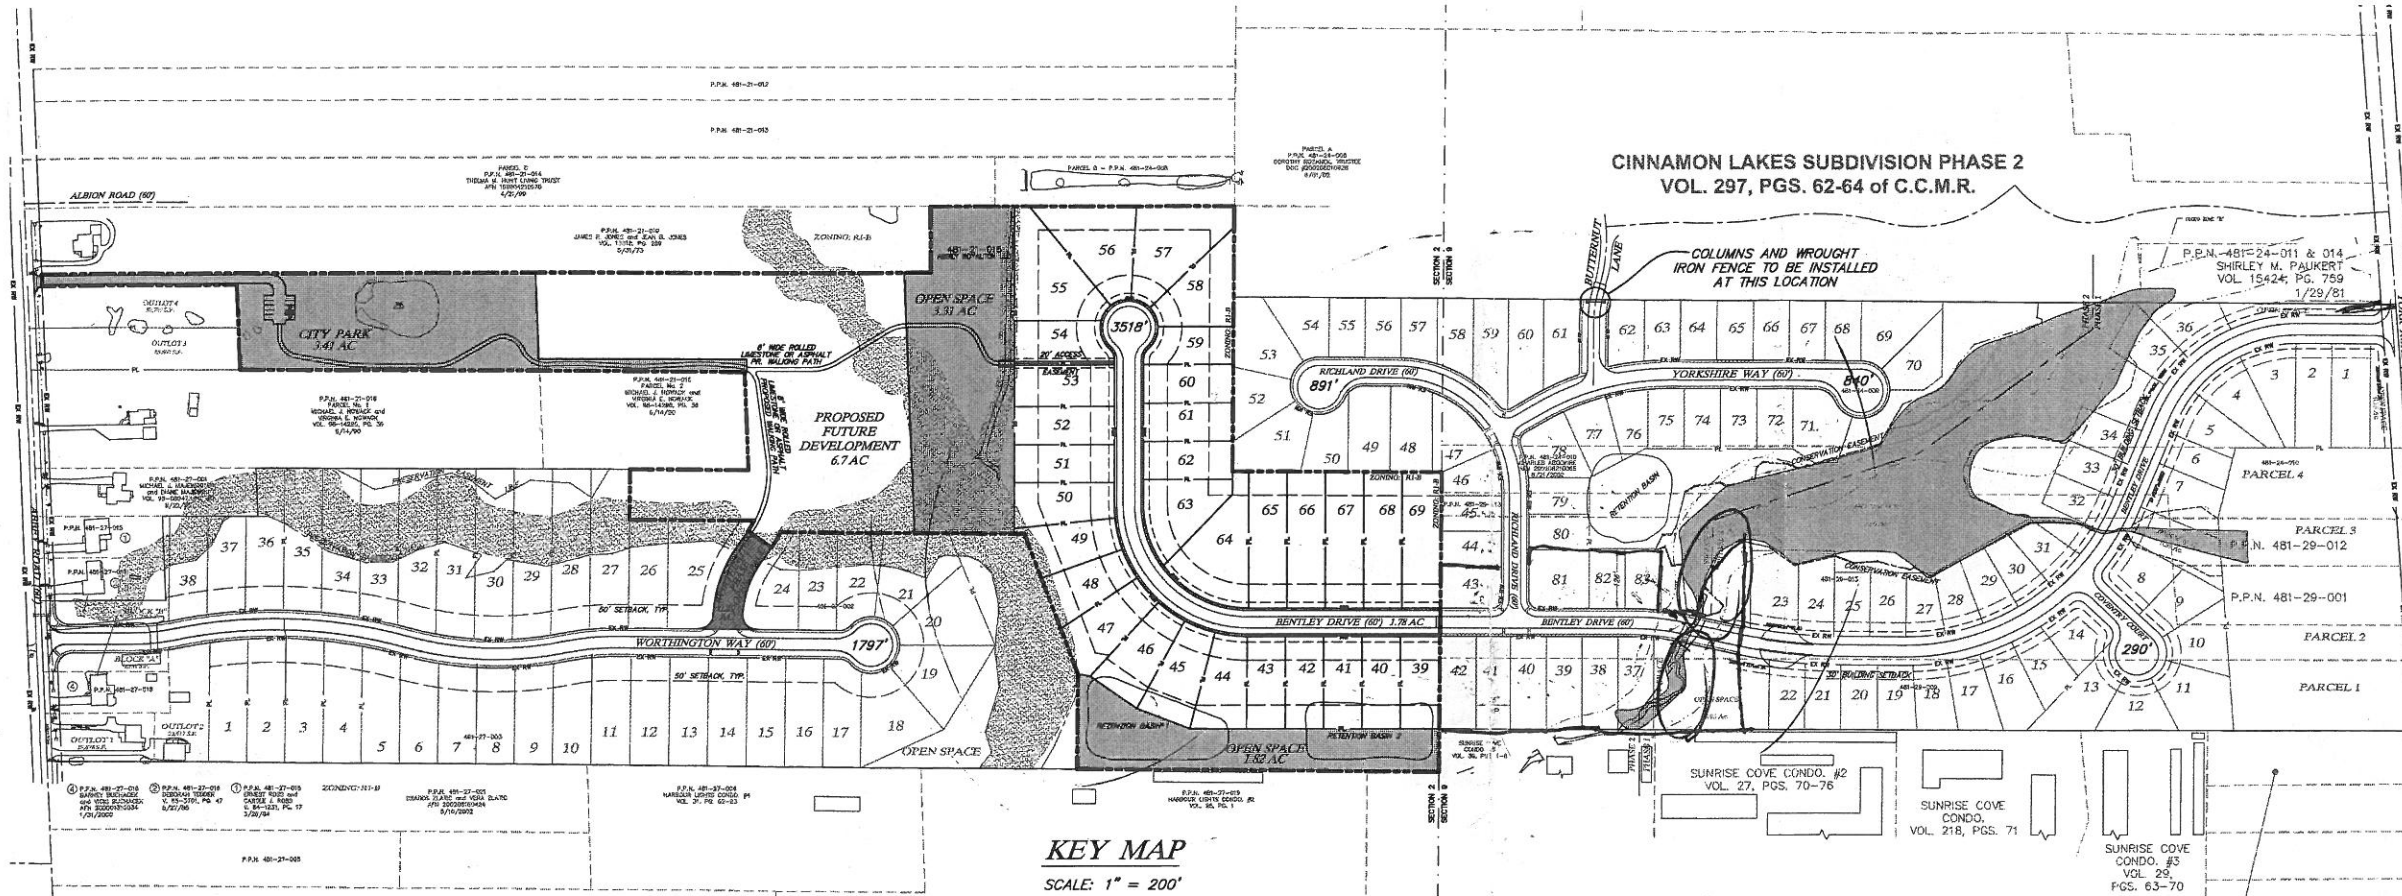


SHEET INDEX

SHEET 1: KEY MAP & SITE INFORMATION
SHEET 2: SITE PLAN



LOCATION MAP
NO SCALE

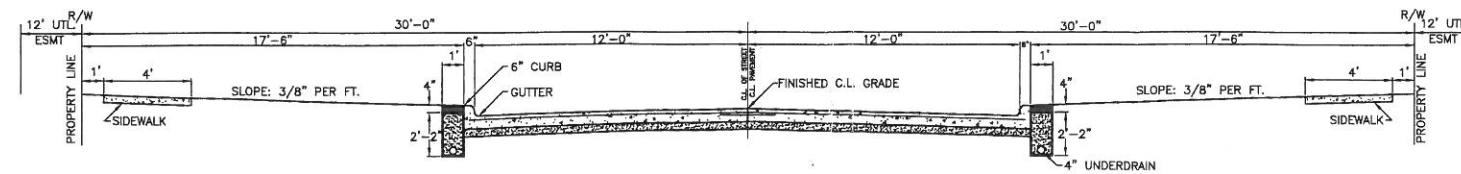

TYPICAL PAVEMENT SECTION
NO SCALE

APPROVAL

THIS PRELIMINARY PLAN APPROVED BY THE PLANNING COMMISSION OF THE CITY OF NORTH ROYALTON, OHIO, THIS _____ DAY OF _____, 2008.

CHAIRPERSON _____ PRINT NAME _____
SECRETARY _____ PRINT NAME _____

WORTHINGTON PHASE II
REVISED
PRELIMINARY PLAT

TGC Engineering, LLC
387 MEDINA ROAD, SUITE 500
MEDINA, OH 44256
(PHONE) 330.590.8004 (FAX) 330.239.6200

PROJECT NO.
1047
DATE
NOV. 7, 2008

1
2